


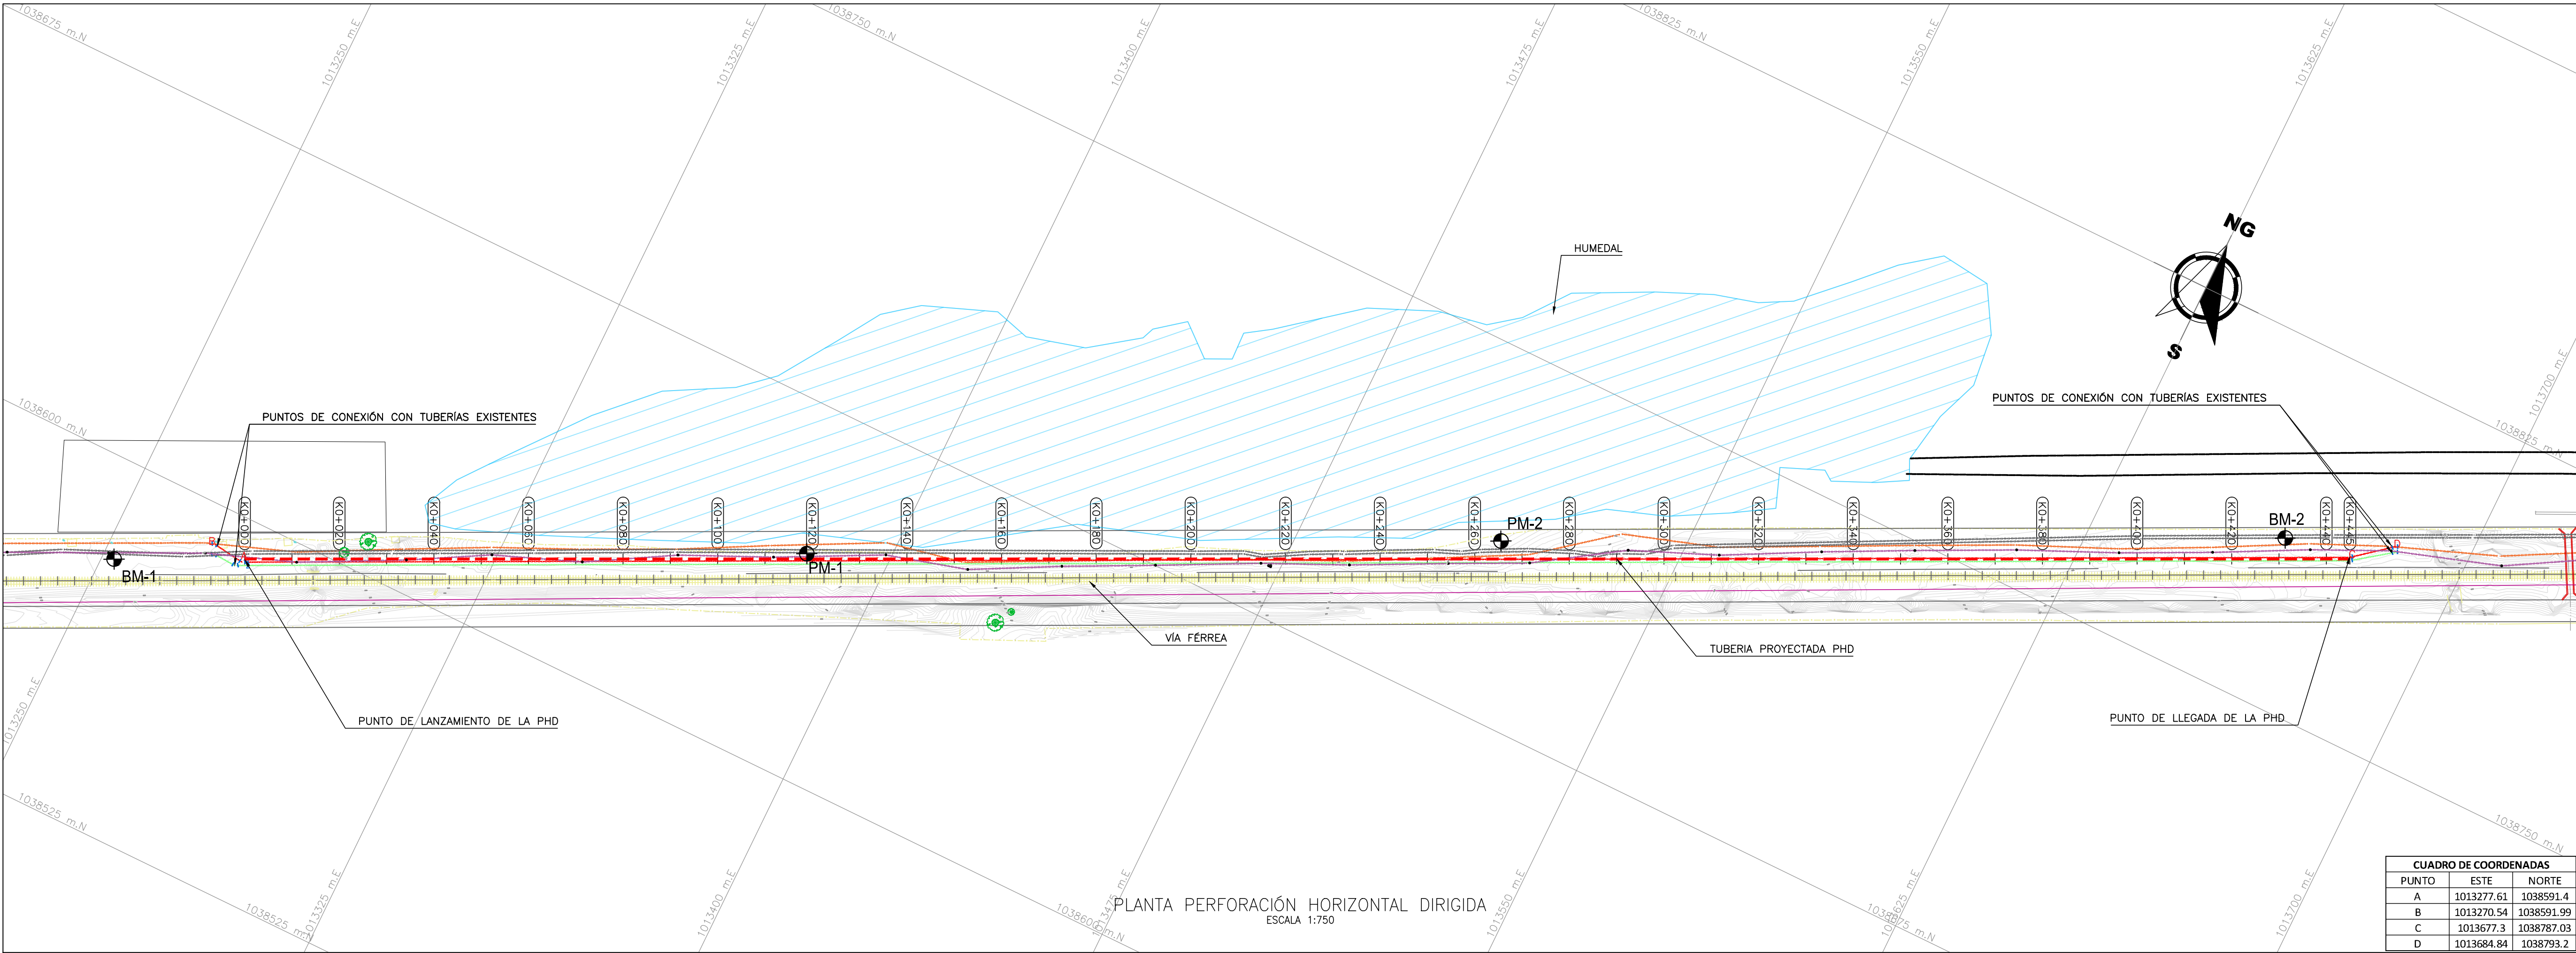

LOCALIZACIÓN GENERAL

NOTAS

1. SISTEMA DE COORDENADAS ORIGEN NACIONAL.

2. TODAS LAS DIMENSIONES Y LAS COORDENADAS ESTÁN EN METROS, A MENOS QUE SE INDIQUE OTRA UNIDAD

3. LA INGENIERÍA CIVIL NO ASUME RESPONSABILIDAD POR ERRORES, OMISIONES O DESACTUALIZACIÓN DE INFORMACIÓN PROVENIENTE DE ESTUDIOS TOPOGRÁFICOS, GEOTÉCNICOS, HIDROLÓGICOS O DE OTRAS DISCIPLINAS, SIENDO RESPONSABILIDAD DE QUIEN LA SUMINISTRA.

4. LA CORRECTA UBICACIÓN DE CIMENTACIONES, ESTRUCTURAS, PLATAFORMAS, ACCESOS Y DEMÁS ELEMENTOS DEBERÁ SER VERIFICADA EN SITIO, AJUSTANDO LO NECESARIO PARA GARANTIZAR LA IMPLANTACIÓN ADECUADA, SIN ALTERAR LA INTENCIÓN DEL DISEÑO Y PREVIA NOTIFICACIÓN A LA INTERVENTORIA.

5. EL CONTRATISTA ES RESPONSABLE DE REVISAR Y LOCALIZAR EN CAMPO TODAS LAS INSTALACIONES ENTERRADAS (CABLES, TUBERÍAS, DRENAJES, DUCTOS, SIMILARES) ANTES DE EJECUTAR EXCAVACIONES O FUNDACIONES. CUALQUIER DAÑO A ESTOS ELEMENTOS POR FALTA DE VERIFICACIÓN SERÁ DE SU EXCLUSIVA RESPONSABILIDAD.

6. EL DISEÑO SE HA REALIZADO CON BASE EN LOS RESULTADOS DE ESTUDIOS GEOTÉCNICOS Y DEMÁS INFORMACIÓN TÉCNICA DISPONIBLE, CUYA VALIDEZ CORRESPONDE A LAS ENTIDADES EJECUTORAS; SI LAS CONDICIONES REALES DE TERRENO DIFIEREN DE LAS PREVISTAS, DEBERÁN REALIZARSE LOS ESTUDIOS COMPLEMENTARIOS QUE SE REQUIERAN, ASUMIENDO EL CONTRATANTE LOS AJUSTES DE ALCANCE, COSTO Y PLAZO QUE CORRESPONDAN.


7. TODOS LOS DISEÑOS SE HAN DESARROLLADO CONFORME A LA NORMATIVA TÉCNICA VIGENTE (NSR-10, ACI, ASTM, ICONTEC Y DEMÁS APLICABLES), Y CUALQUIER REQUERIMIENTO ADICIONAL O NORMATIVIDAD ESPECIAL DEBERÁ SER DEFINIDO Y APROBADO POR EL CLIENTE ANTES DE CONSTRUCCIÓN.

8. LAS TOLERANCIAS GEOMÉTRICAS Y DE NIVELACIÓN DEBERÁN AJUSTARSE A LAS ESPECIFICACIONES TÉCNICAS DEL PROYECTO, Y CUALQUIER DESVIACIÓN DEBERÁ SER NOTIFICADA Y APROBADA POR LA INTERVENTORIA.

9. LA VERSIÓN DIGITAL DE ESTE DOCUMENTO PREVALECE SOBRE CUALQUIER IMPRESIÓN FÍSICA, Y ESTA PROHIBIDO USAR EL PRESENTE PLANO PARA FINES DISTINTOS A LOS DEFINIDOS EN EL ALCANCE DE LA INGENIERÍA DE DETALLE SIN AUTORIZACIÓN EXPRESA DEL DISEÑADOR.

CUADRO DE COORDENADAS

PUNTO	ESTE	NORTE
A	1013277.61	1038591.4
B	1013270.54	1038591.99
C	1013677.3	1038787.03
D	1013684.84	1038793.2

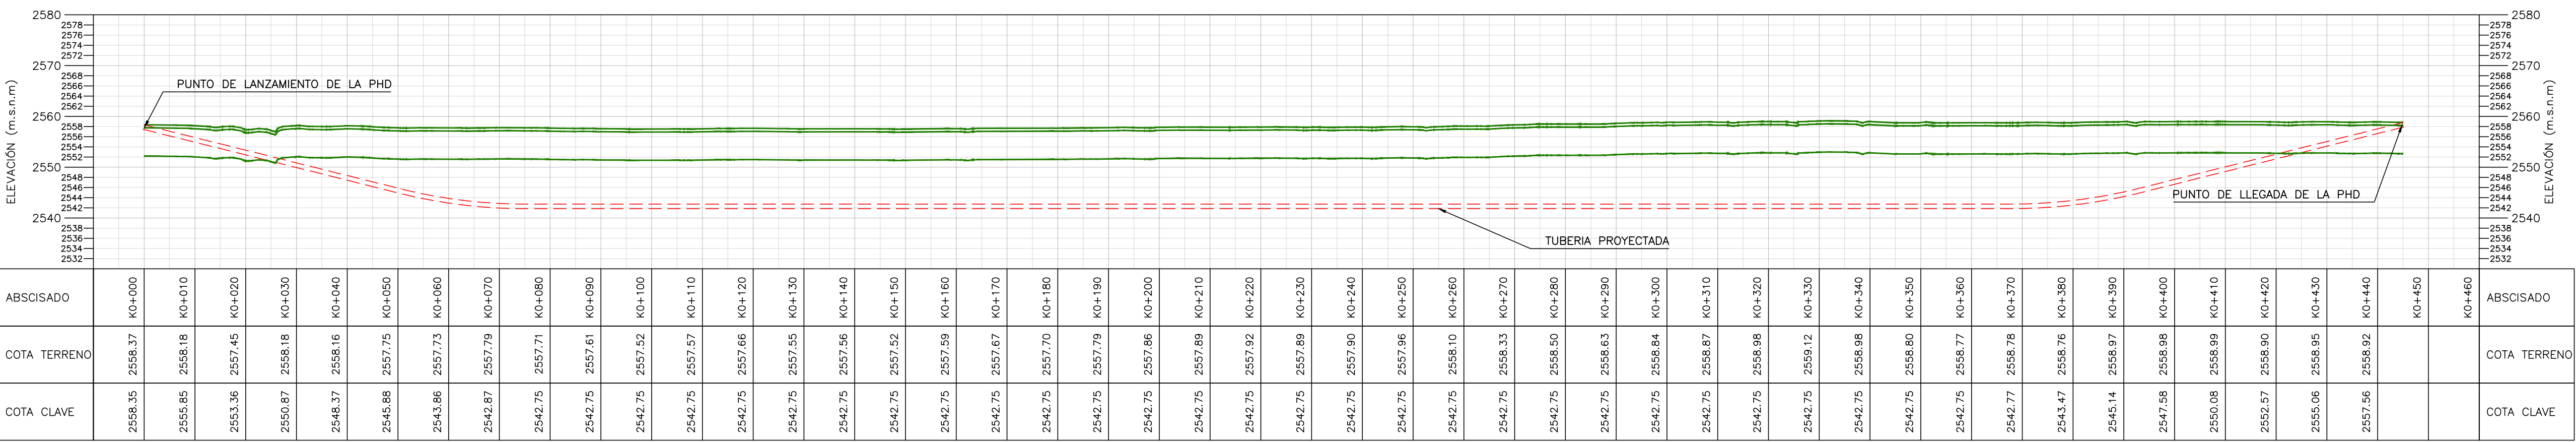

CONVENCIONES

CONDUCCIÓN SALMUERO (NUEVO)

CONDUCCIÓN CONDENSADO (NUEVO)

CONDUCCIÓN SALMUERO (EXISTENTE)

CONDUCCIÓN CONDENSADO (EXISTENTE)

CERCA DE ALAMBRE

VIA FÉRREA

CURVA DE NIVEL

PLANOS DE REFERENCIA

Brinsz

cinecon

PROYECTO:

REUBICACIÓN DE REDES POR PERFORACIÓN HORIZONTAL DIRIGIDA EN CRUCE HUMEDAL PARQUE JAIME DUQUE FASE 4

TÍTULO:

PLANO PLANTA – PERFIL ÁREA DE CONEXIÓN

LIBRO:

BRINSA

FIRMA:

DISEÑO:

JEISON JIMÉNEZ

REVISÓ:

ARTURO GÓMEZ

APPROBO:

GUSTAVO BONILLA

DIBUJO:

JEISON JIMÉNEZ

FECHA:

11-JUN-26

ESCALA:

1:750

PLANO No.

202609-BRI-SE-CIV-PL-001

HOJA:

1 DE 1

REV:

RB

PERFIL PERFORACIÓN HORIZONTAL DIRIGIDA
ESCALA 1:750

